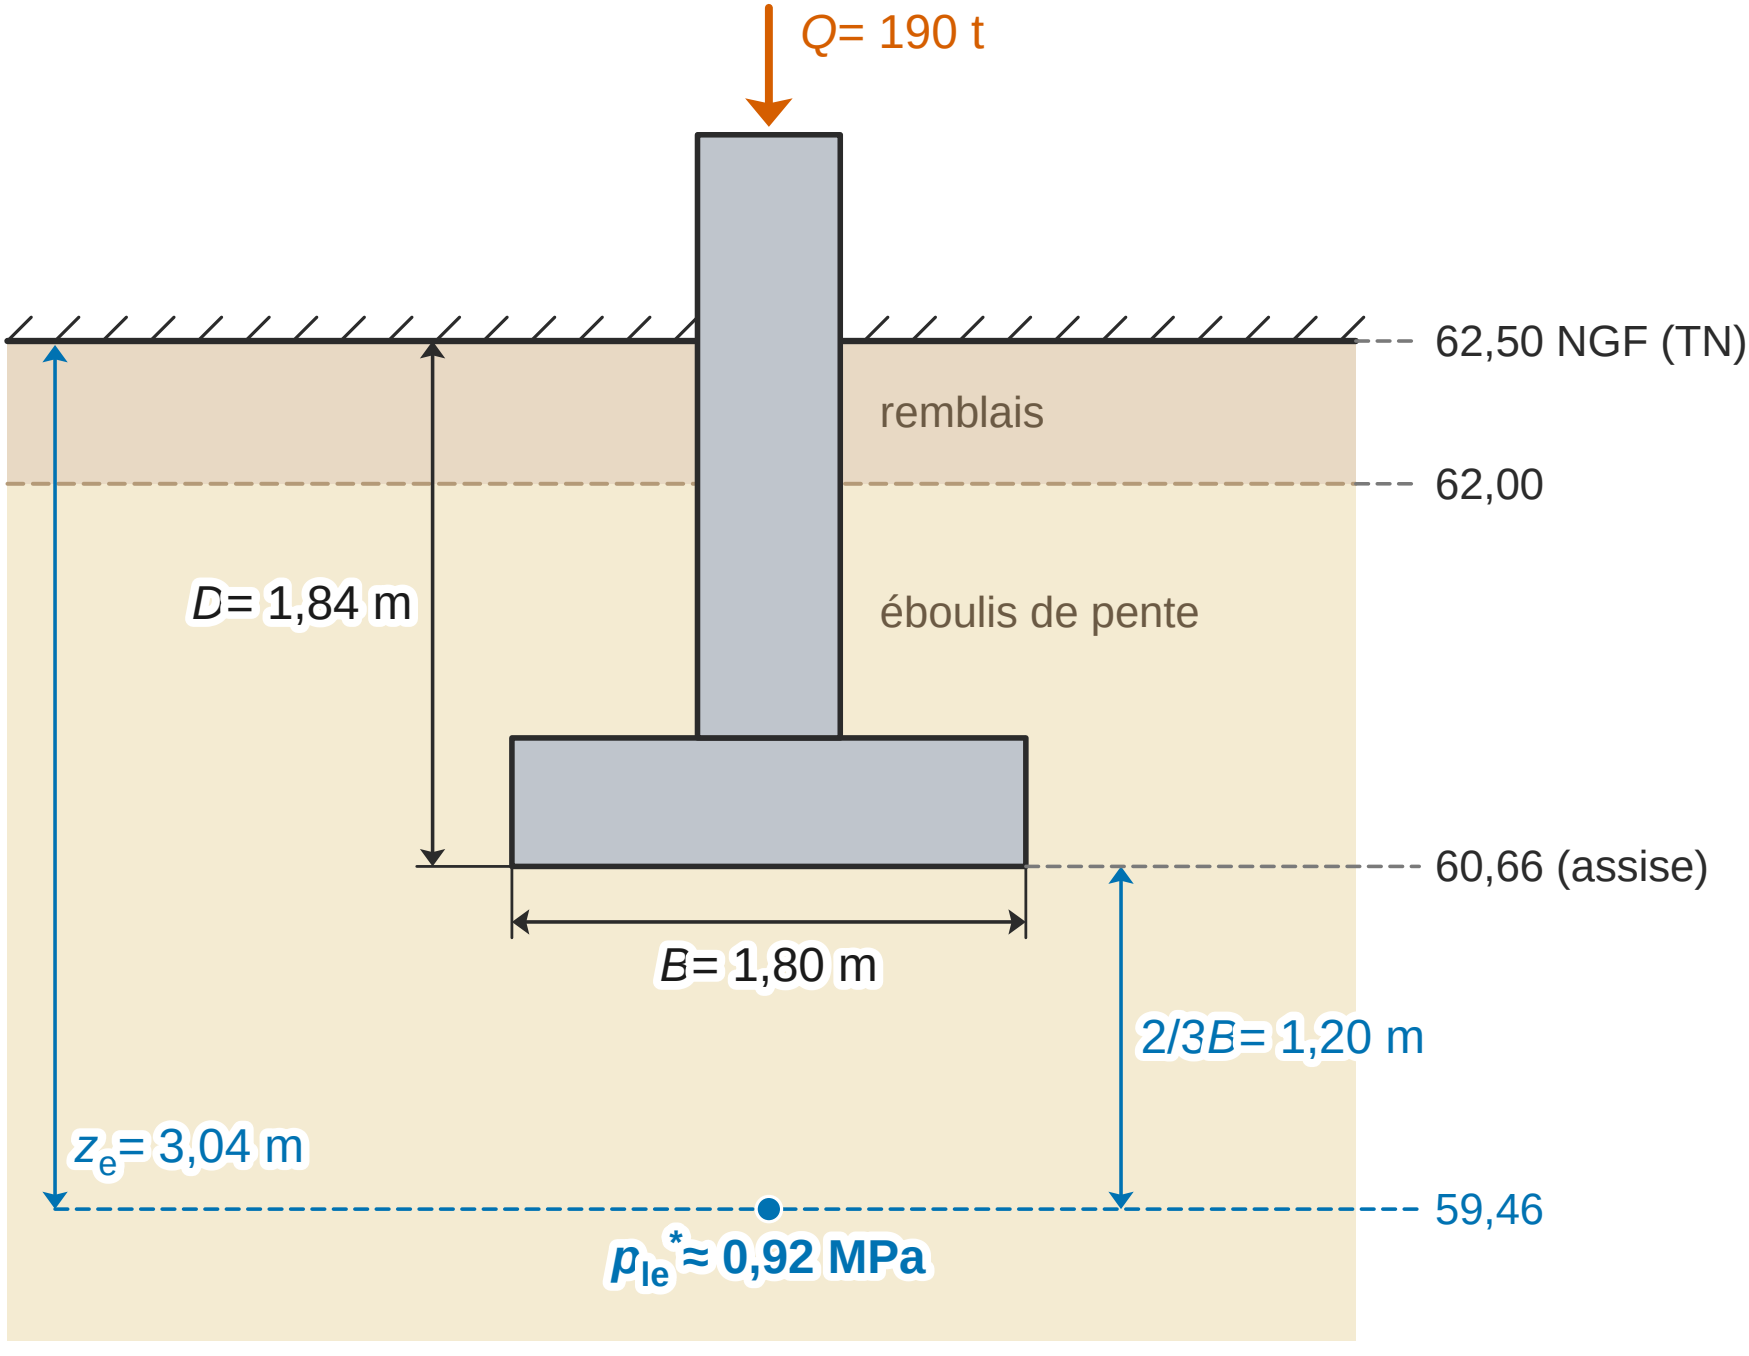
Q= 190 t
62,50 NGF (TN)
remblais
62,00
D= 1,84 m
éboulis de pente
60,66 (assise)
B= 1,80 m
2/3B= 1,20 m
z_e= 3,04 m
59,46
p_le*≈ 0,92 MPa